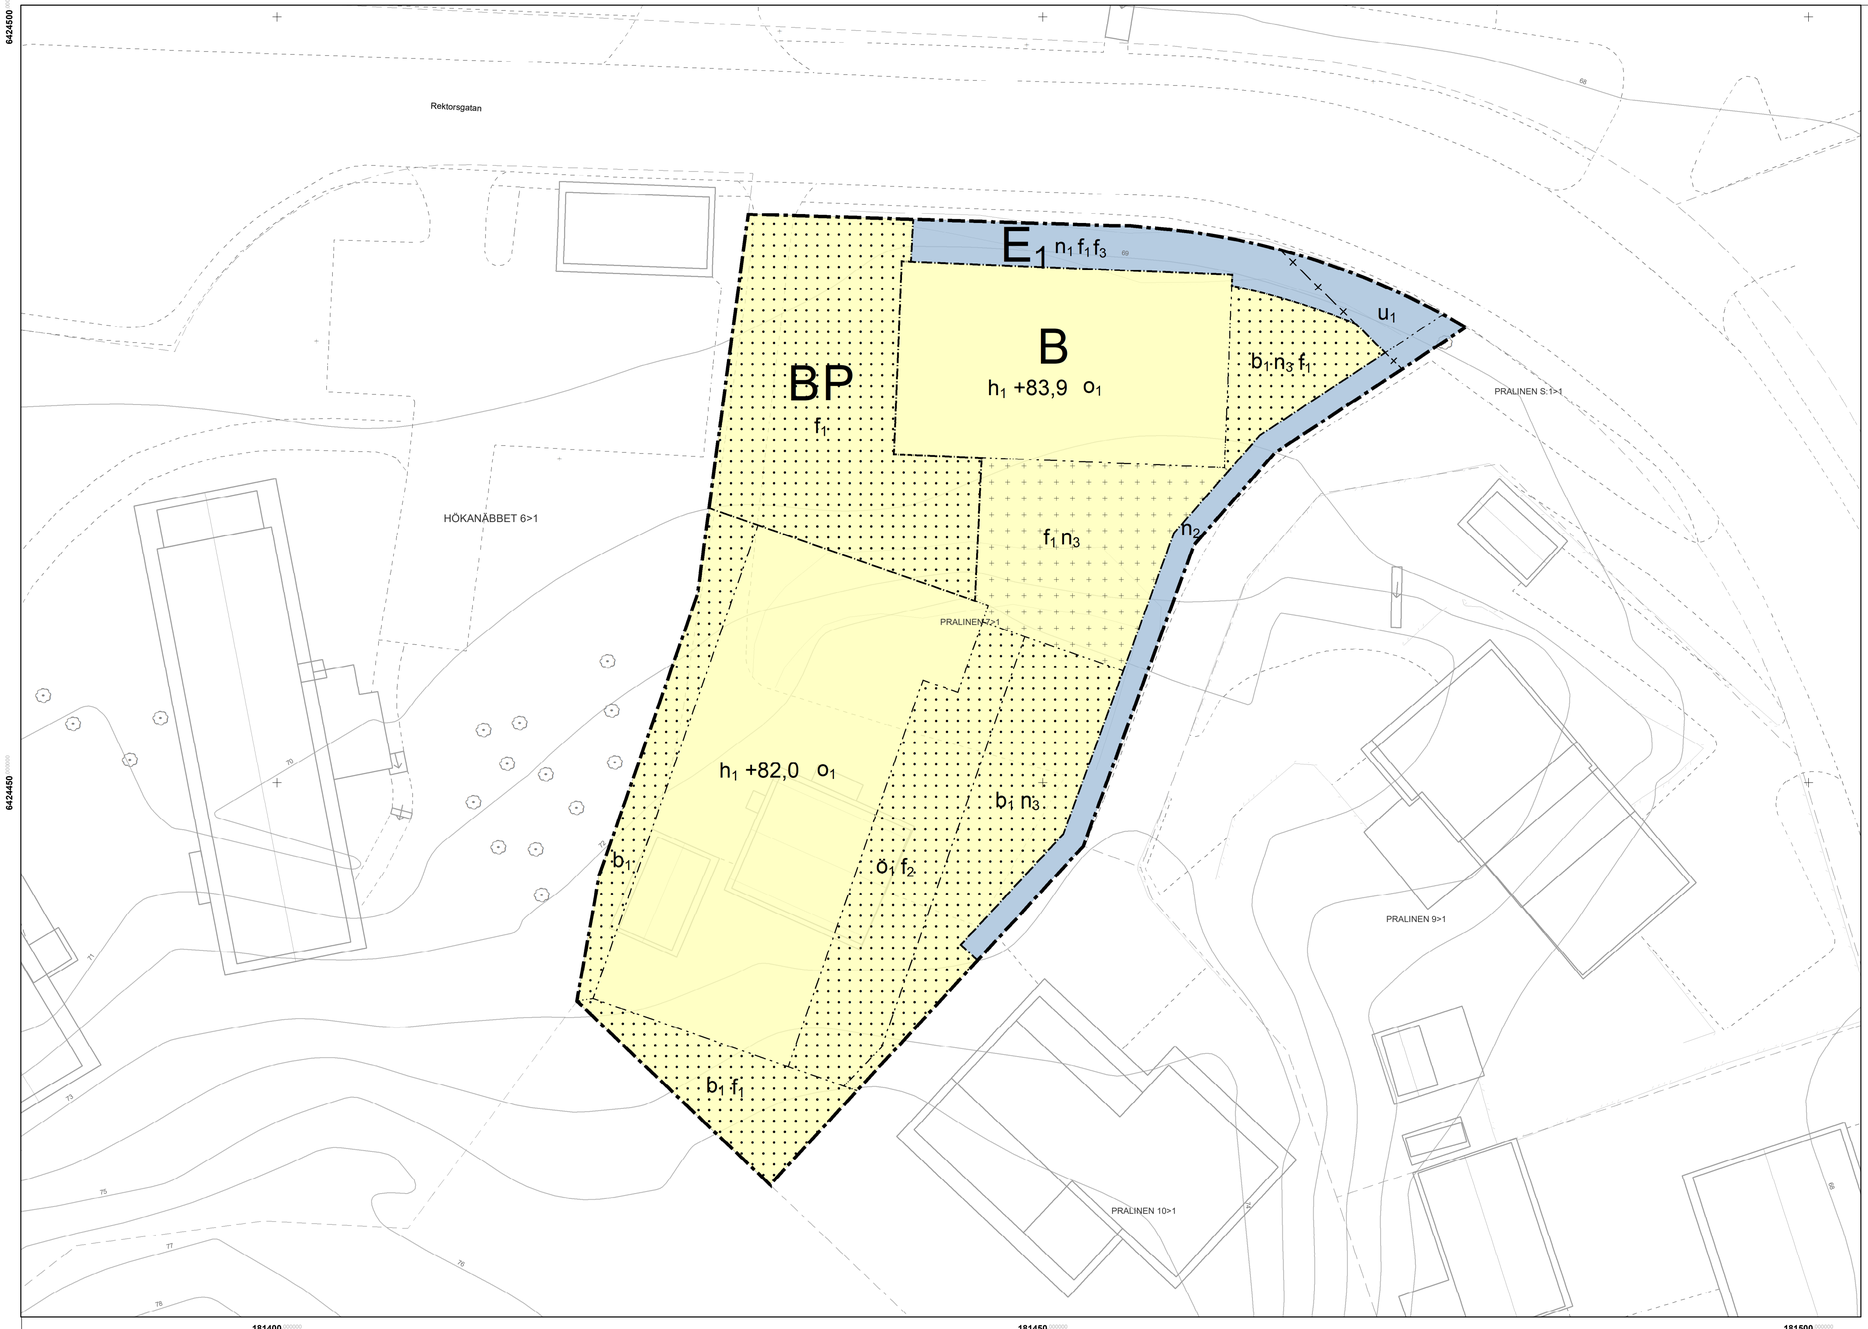


PLANBESTÄMMELSER

Följande gäller inom områden med nedanstående beteckningar.

Endast angiven användning och utformning är tillåten.

Där beteckning saknas gäller bestämmelsen inom all kvartersmark eller all allmän plats eller allt vattenområde på plankartan.

GRÄNSLINJER

- Planområdesgräns
- Användningsgräns
- Egenskapsgräns
- Sekundär egenskapsgräns

ANVÄNDNING AV KVARTERSMARK

B	Bostäder
E_1	Dagvattenanläggning
P	Parkering

EGENSKAPSBESTÄMMELSER FÖR KVARTERSMARK

Begränsning av markens utnyttjande

	Marken får inte förses med byggnad.
$ö_1$	Endast parkering under mark.
	Marken får endast förses med en komplementbyggnad maximalt 4 meter hög och 30 kvadratmeter stor, placering får ej omöjliggöra drift och underhåll av öppet dagvattendike.

Höjd på byggnadsverk

h_1 +0,0	Högsta nockhöjd är angivet värde i meter över angivet nollplan.

Markreservat för allmännyttiga ändamål

u_1	Markreservat för underjordiska ledningar (begränsas av sekundär egenskapsgräns)

Takvinkel

o_1	Tak ska utformas som ett sadeltak med en takvinkel mellan 20 och 35 grader, takkupor undantas från denna bestämmelse.

Markens anordnande och vegetation

n_1	Biofilter med ett djup om ca 1 meter och lägsta utlopp vid +67,05 som omhändertar och renar dagvatten från parkering och angöringsyta ska anläggas.
n_2	Öppet dike med ett djup om ca 0,15 meter och lägsta utlopp vid +67,00 som omhändertar takvatten från den södra byggnaden ska anläggas. Stödmur tillåts och avåkningsskydd ska anordnas.
n_3	Bilparkering får inte anordnas.

Närmast fasad ska marken ha en lutning på minst 5 %, därefter ska marken luta minst 2 % för att respektive marknivå ska avvattnas till avsedda dagvattenanläggningar.

Utförande

b_1	Minst 80% av marken ska vara genomsläpplig.

Utformning

f_1	Balkong får kraga ut maximalt 1,7 meter från fasadlivet.
f_2	Loftgång får kraga ut maximalt 2 meter från fasadlivet.
f_3	Skärmtak får kraga ut maximalt 1,2 meter från fasadlivet.

GENOMFÖRANDETID

Genomförandetiden är 10 år över hela planområdet och börjar gälla fr.o.m. laga kraft datum.

Grundkartebeteckning

Fastighetsgräns	Fastighetsbeteckning
Traktgräns	Strandlinje
Byggnad	Träd
Vägkant	Elskåp
Järnväg	Belysningsstolpe
Slänt	Höjdkurvor
Staket, Mur	

Grundkartan är upprättad av Samhällsbyggnadsförvaltningen i Alingsås kommun, aktualitetsdatum 2026-07-07.
Inmätning av fastighetsgränser genomförd 2025-09-29.

Koordinatsystem i plan: SWEREF99 12 00
Höjdsystem: RH 2000

0 5 10 20 Meter

Skala 1:200 (A1)
Skala 1:400 (A3)

N

ALINGSÅS KOMMUN

PLANKARTA
ANTAGANDEHANDLING

DETALJPLAN FÖR PRALINEN 7, REKTORSGATAN

Alingsås den 17 september

D.nr: 2024.202 KS

Beslutsdatum	Instans
Samråd	
2026-02-02	KS
Granskning	
2026-05-20	KS
Antagande	
2026-10-19	KS
Laga kraft	

Lovisa Grahn
Planarkitekt

Åsa Jönsson
Planchef